
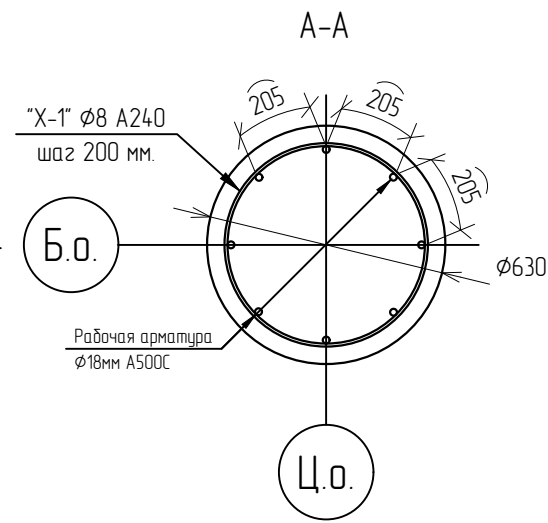
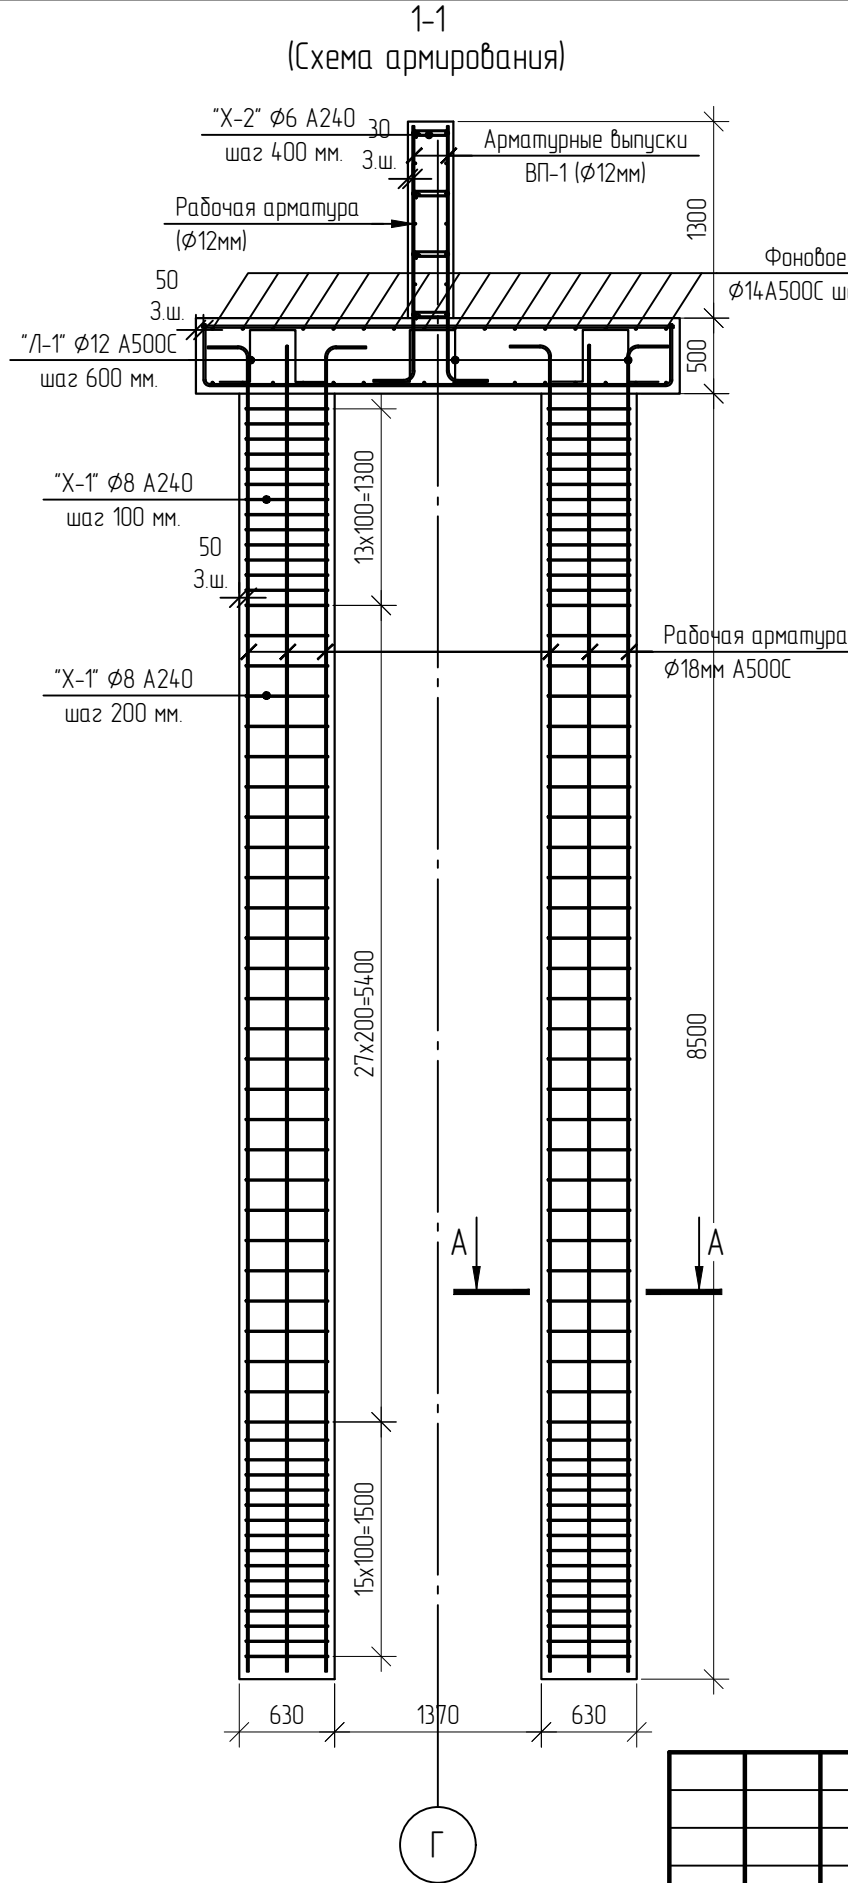


Согласовано		Взам. инв. №	Подп. и дата	Инв. № подл.

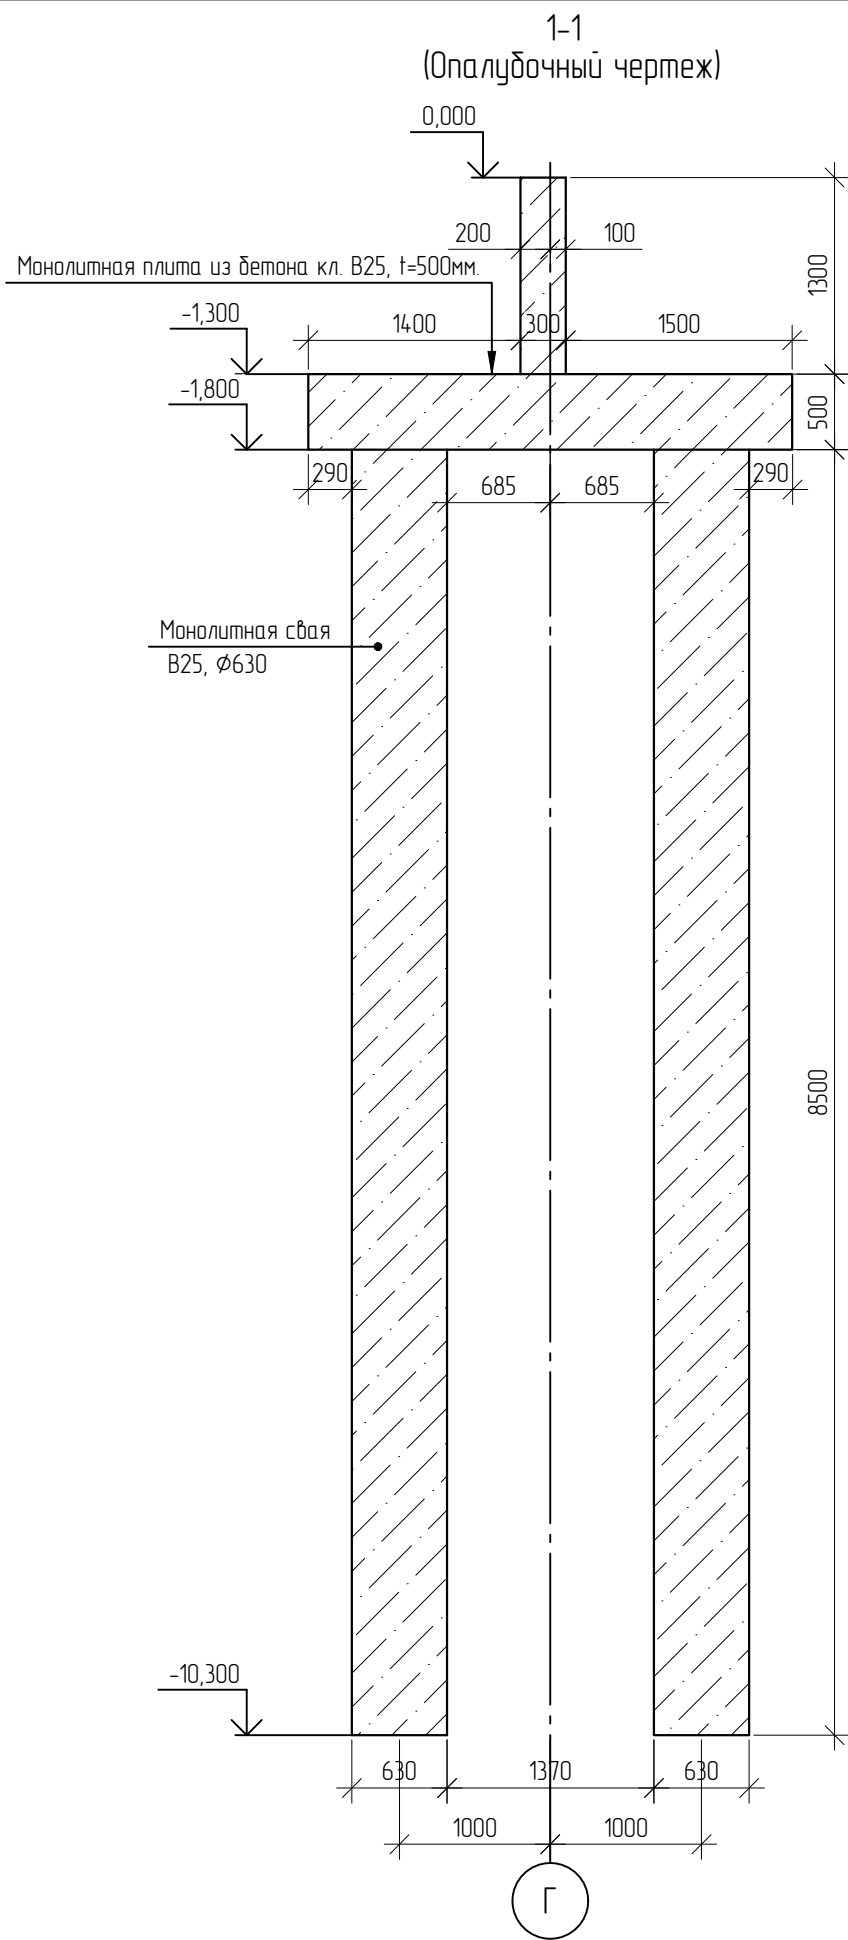

						№04/05-2026-КР		
						Строительство складского комплекса, расположенного по адресу: Республика Крым, городской округ Симферополь, город Симферополь (Кад. номер: 90.22.010215.6931)		
Изм.	Кол. уч.	Лист	№ док.	Подп.	Дата	Конструктивные решения	Стадия	Лист
Разработал	Вейсов Д.И.						П	3
Проверил	Вейсов Д.И.							
ГИП	Силиамиев С.Р.							
Директор	Вейсов Д.И.					1-1, Узел А	ООО "Мимар", г. Симферополь	