
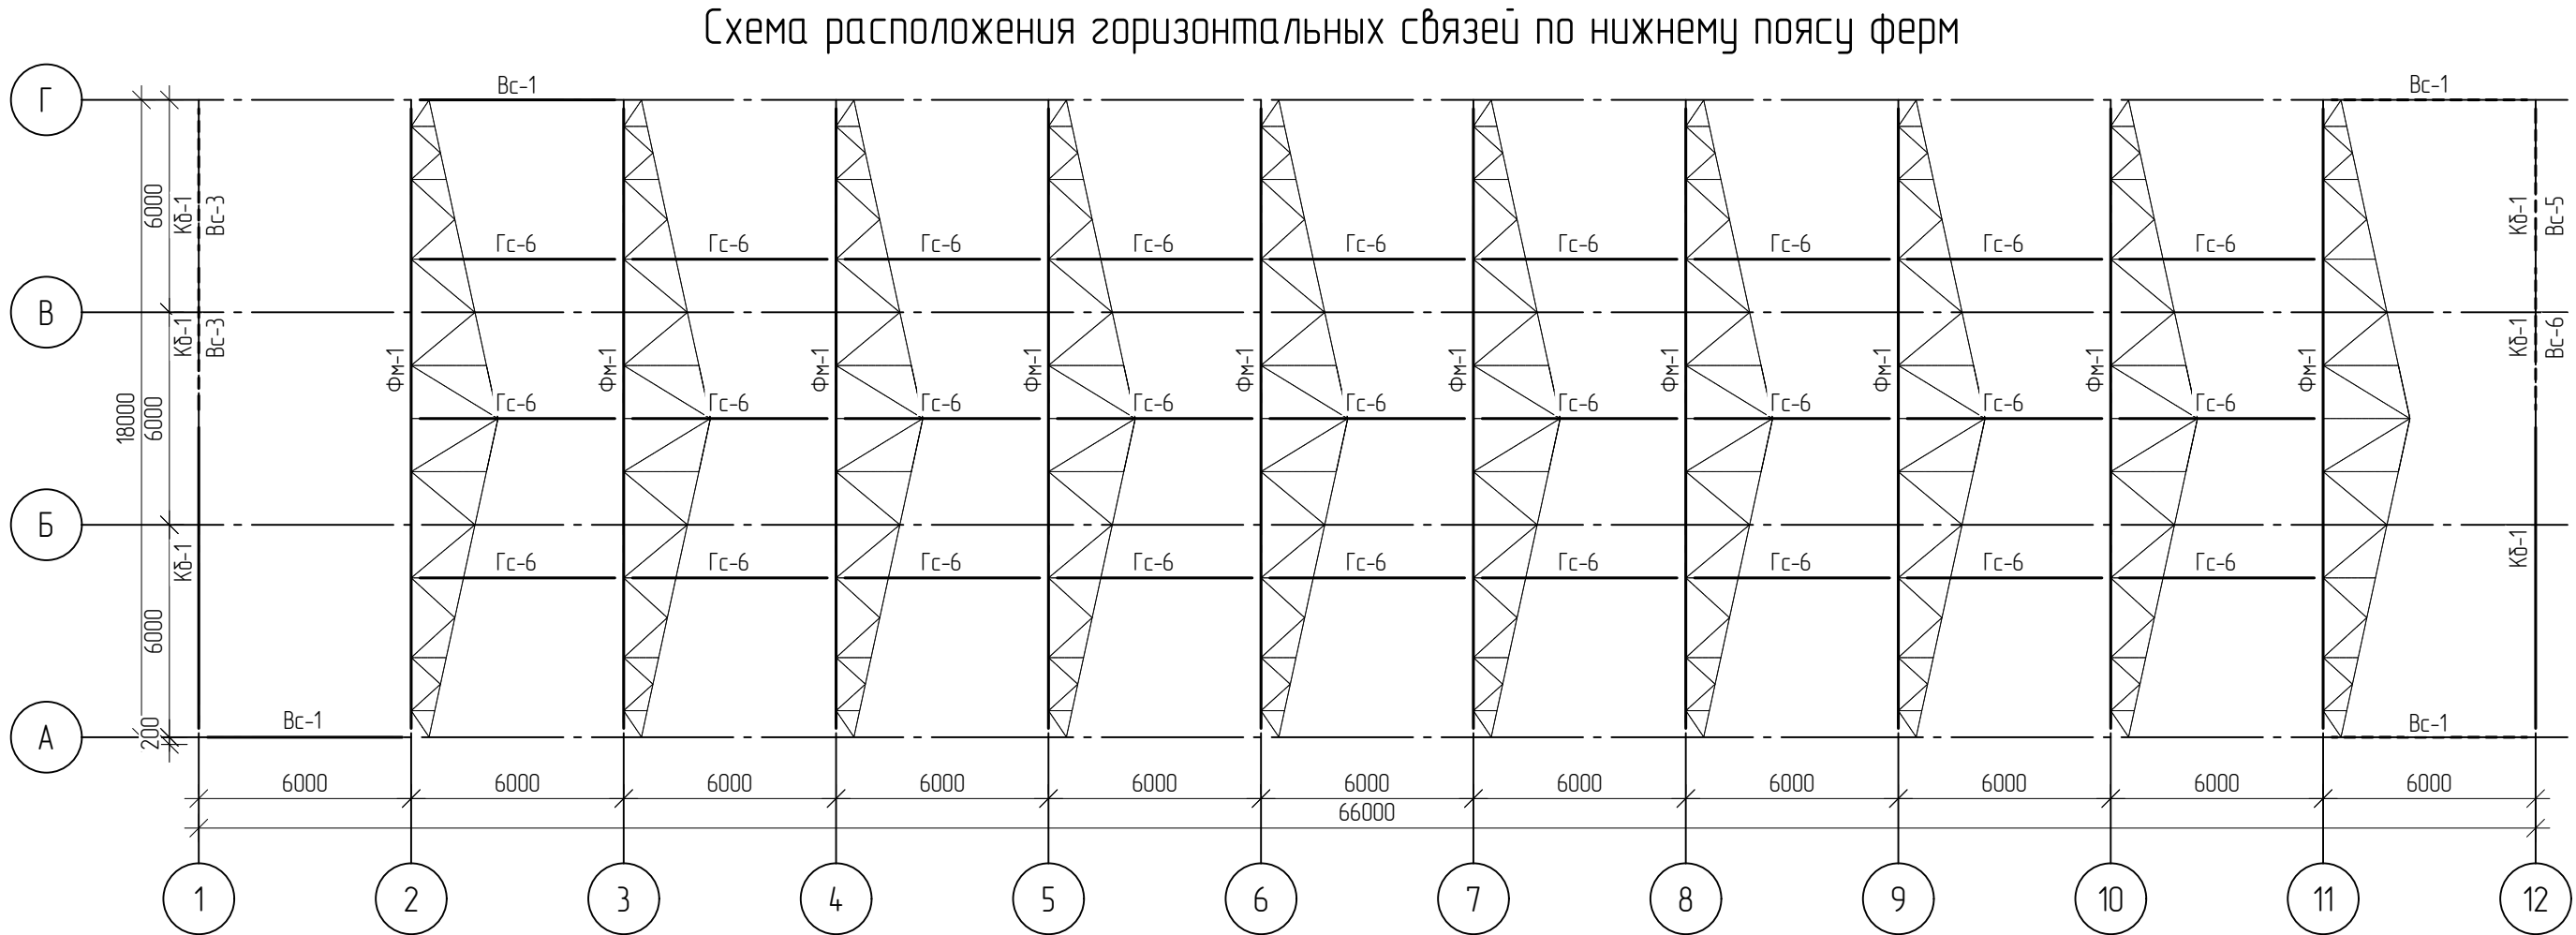


Согласовано		
Взам. инв. №		
Подп. и дата		
Инв. № подл.		

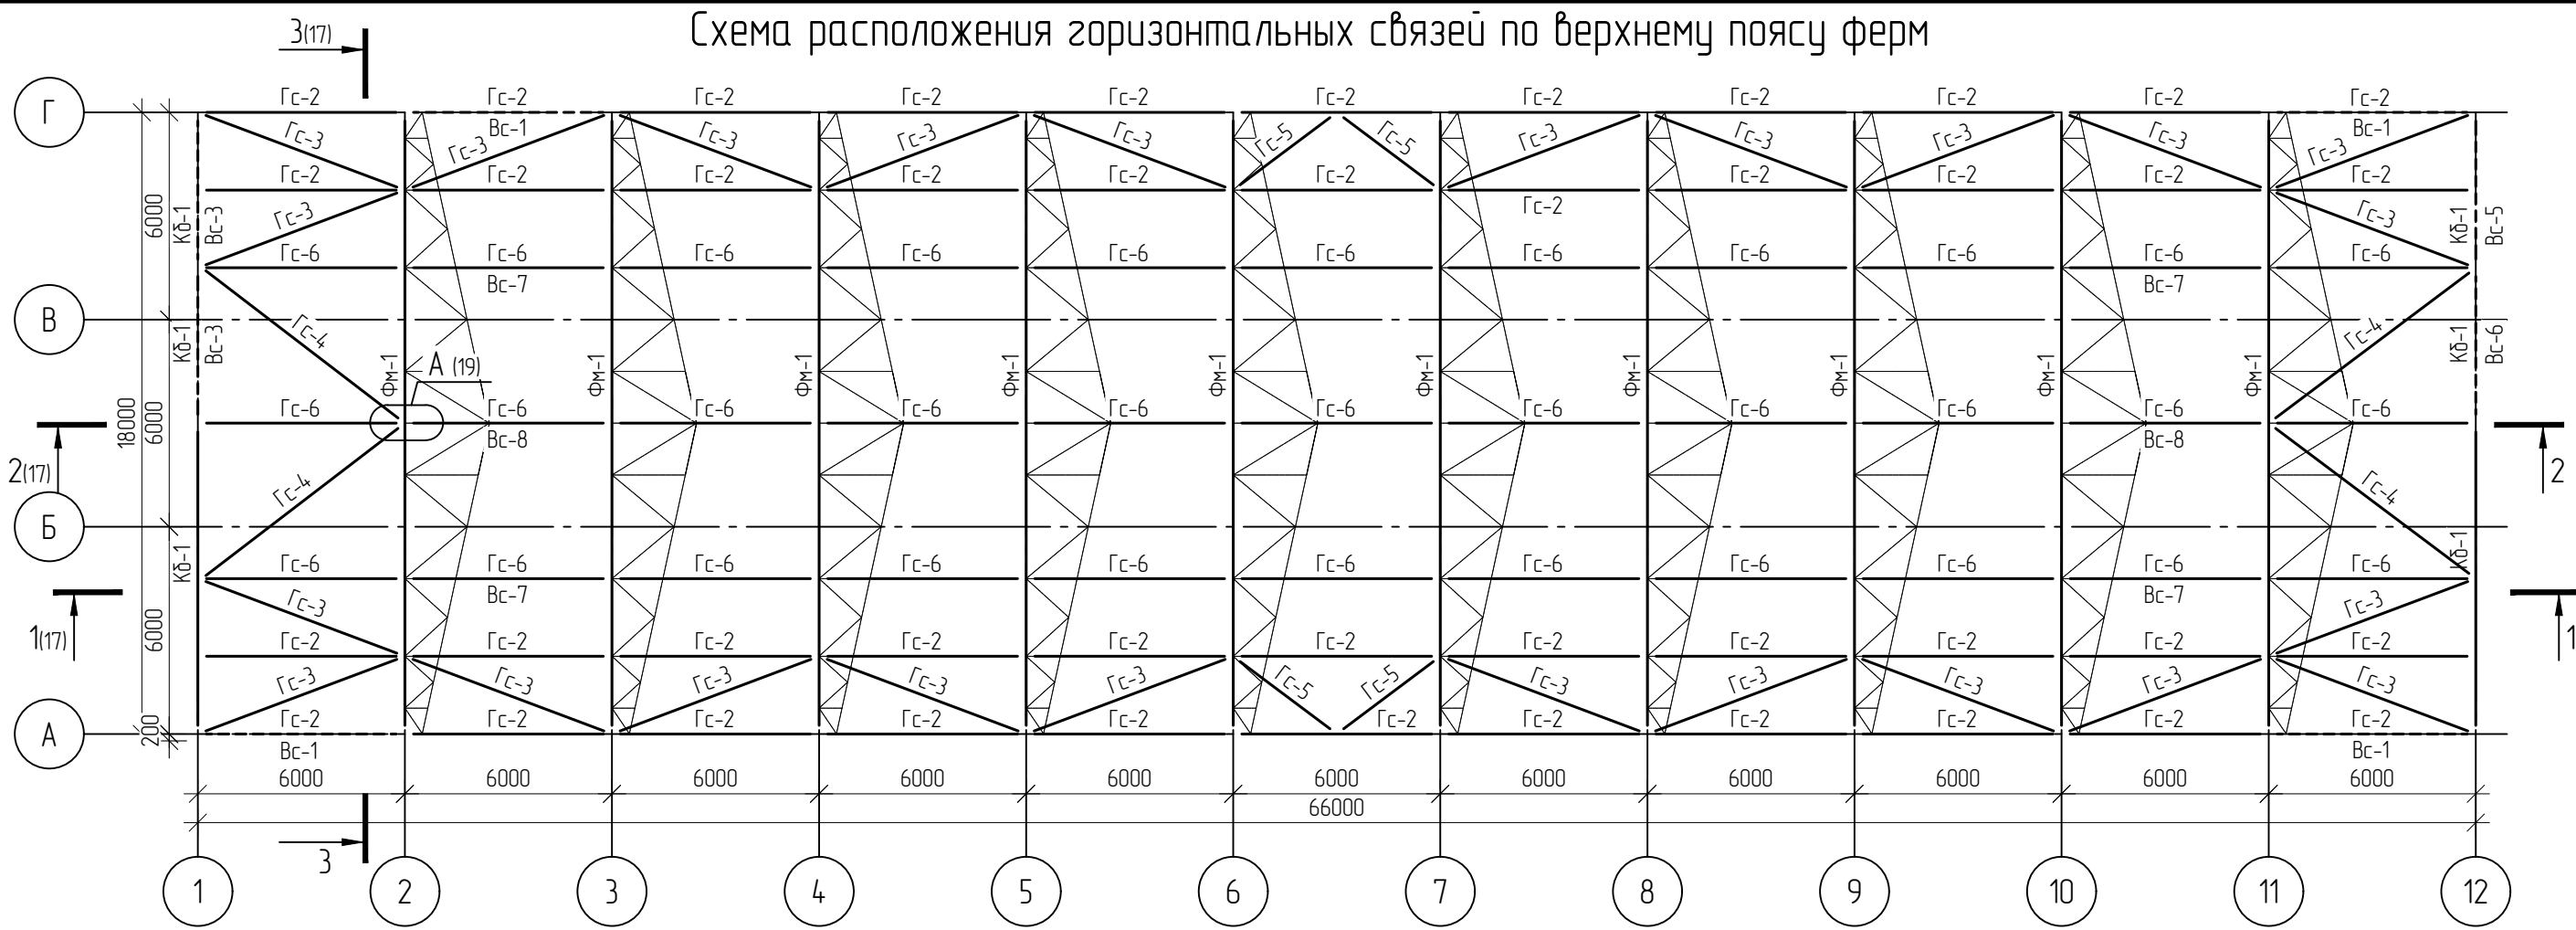

Спецификация на металлические фермы				
Поз	Обозначение	Наименование	Кол	Масса, ед., кг
Фм-1	см. л. 18,19	Ферма 1	10	
Вс-1	см. л. 8	С3140x5 мм	8	
Вс-2	см. л. 8	С3140x5 мм	8	
Вс-3	см. л. 9	С3140x5 мм	2	
Вс-4	см. л. 10	С3120x5 мм	4	
Вс-5	см. л. 10	С3100x5 мм	2	
Вс-6	см. л. 10	С3100x5 мм	2	
Вс-7	см. л. 17	С360x3 мм	8	
Вс-8	см. л. 17	С360x3 мм	4	
Гс-1	Горизонтальная связь 1	С3180x5 мм	6	
Гс-2	Горизонтальная связь 2	С3120x4 мм	44	
Гс-3	Горизонтальная связь 3	С3120x4 мм	24	
Гс-4	Горизонтальная связь 4	С3120x4 мм	4	
Гс-5	Горизонтальная связь 5	С3120x4 мм	4	
Гс-6	Горизонтальная связь 6	С3100x4 мм	60	
Кд-1	Крайняя балка 1	С3160x4 мм	4	

							№04/05-2026-КР				
							Строительство складского комплекса, расположенного по адресу: Республика Крым, городской округ Симферополь, город Симферополь (Кад. номер. 90.22.010215.6931)				
Изм.	Кол. уч.	Лист	№ док.	Подп.	Дата		Конструктивные решения		Стадия	Лист	Листов
Разработал	Вейсб Д.И.						Схема расположения горизонтальных связей по верхнему/нижнему поясу ферм		П	16	
Проверил	Вейсб Д.И.										
ГИП	Сиямиев С.Р.										
Директор	Вейсб Д.И.								ООО "Мимар", г. Симферополь		