


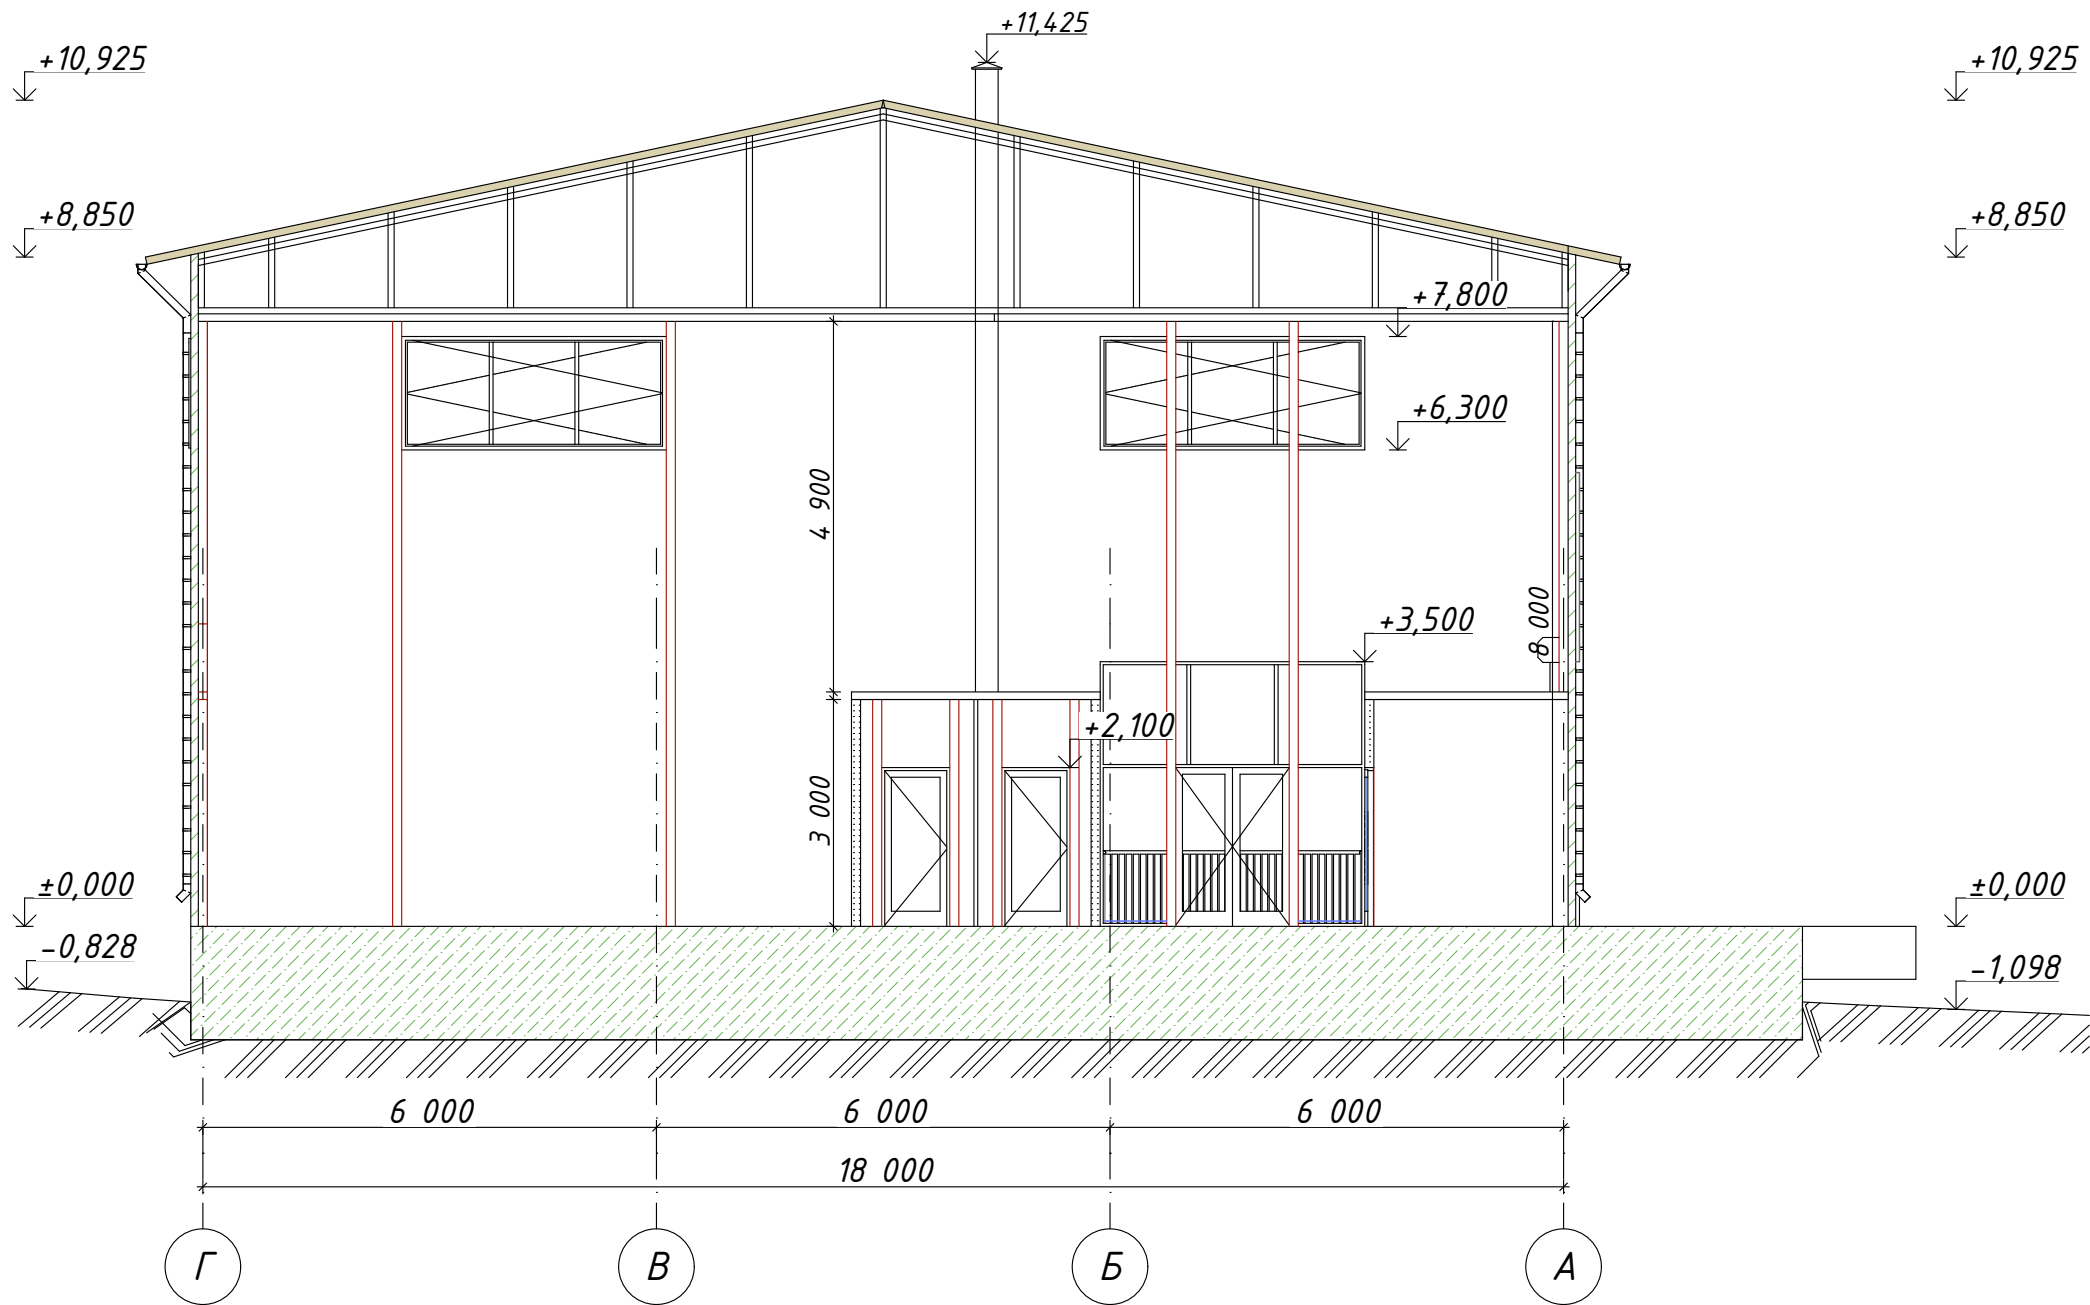

Примечание:
За относительную отметку 0,000 принята отметка чистого пола первого этажа, что соответствует абсолютной отметке 331,50

						№04/05-2026-КР		
						Строительство складского комплекса, расположенного по адресу: Республика Крым, городской округ Симферополь, город Симферополь (Кад. номер: 90:22:010215:6931)		
Изм.	Колуч	Лист	№Док.	Подп.	Дата		Стадия	Лист
Разработал	Мусаева					Конструктивные решения	П	26
Н.контроль	Сиямяев							
ГИП	Вейсов							
Директор	Вейсов					Разрез 1-1 (поз. по ГП 1), М 1:100	MIMAR проектирование оформление ООО "Мимар" г.Симферополь	